


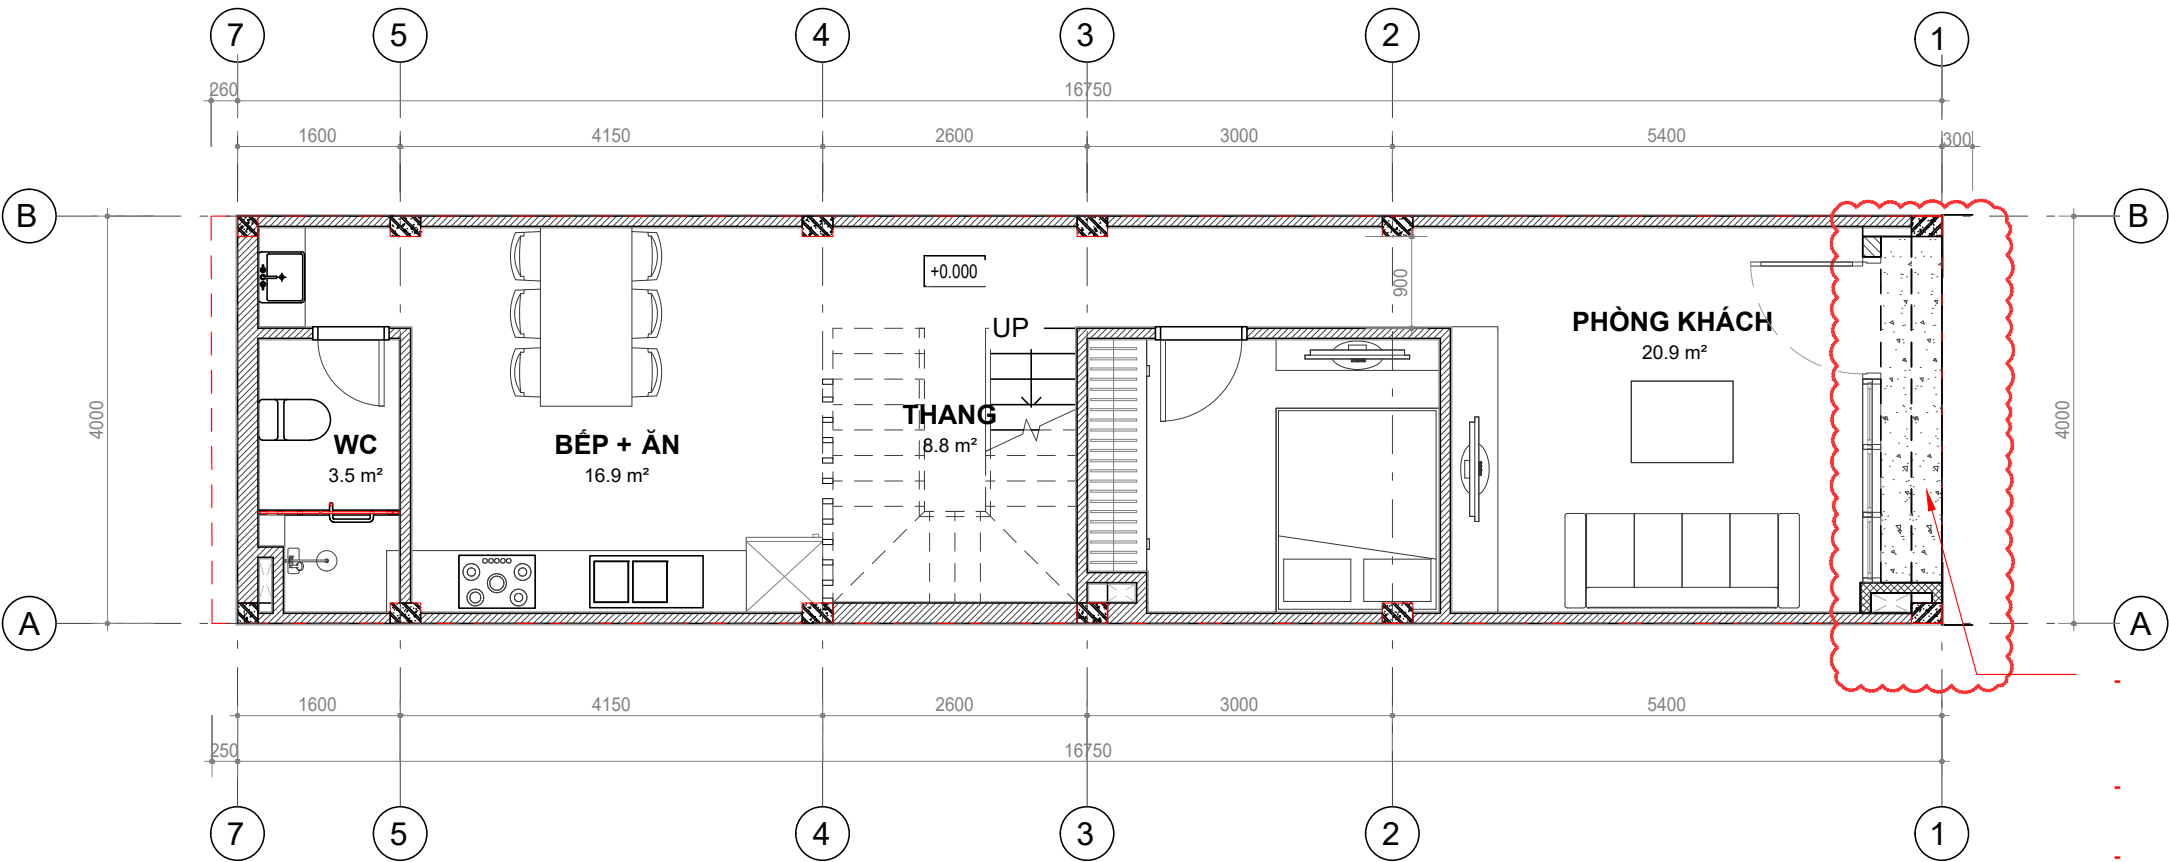

- THAY ĐỔI KHOẢNG LÙI: LÙI VÀO 600 SO VỚI CHỈ GIỚI VÀ RANH GIỚI LỘ ĐẤT
- HỆ KẾT CẤU CỘT GIỮ NGUYÊN THEO THIẾT KẾ CŨ
- THAY ĐỔI THIẾT KẾ CỬA CHÍNH

1 MẶT BẰNG TẦNG 1
A2.01 1 : 75

CONCEPT DRAWING

Drawing Title

Drawn By		Date	
Checked By			
Scale		Sheet No.	
CAD Ref.		REV	
Drawing No.			

©2023, Studio Milou Singapore Pte Ltd reserves all rights to these drawings, designs and/or any other data contained herein. No part of the said drawings, designs and/or other data may be reproduced, modified, transmitted or used in any form or by any means for any purpose without the prior written consent of studioMilou singapore Pte Ltd other than the sole purpose for which such drawings, designs and/or other data are provided to licensed users on such terms as studioMilou singapore Pte Ltd may prescribe.